


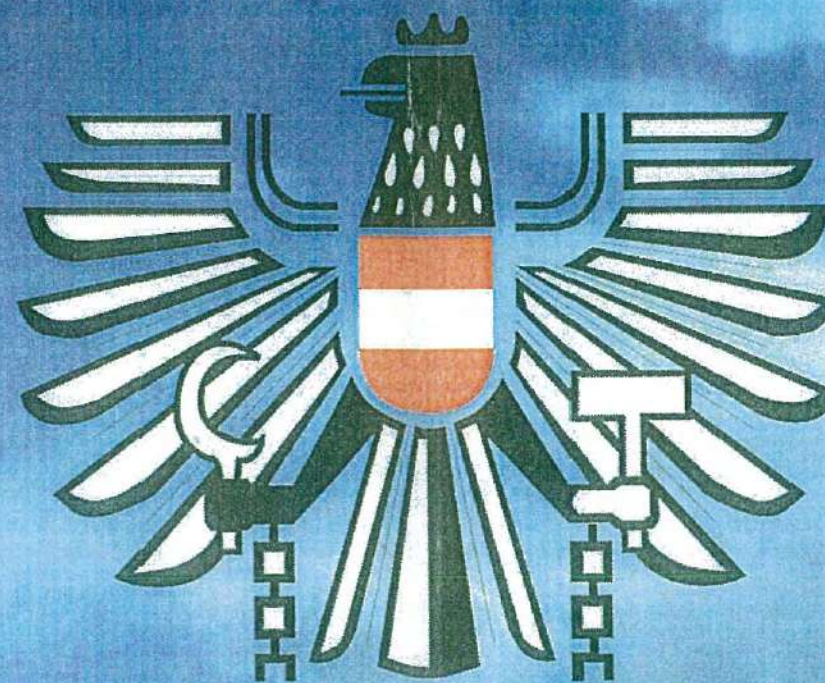

NEUBAU WOHNHAUS DR. TRIFU
EINREICHUNG GZ: 26500

6.6..2007
INDEX A

MAßSTAB 1/100
A3-FOLDER

ARCHITEKTEN CSERNI & PAUGGER ZIVILTECHNIKER GmbH



STAATLICH BEFUGTE UND BEEIDETE ZIVILTECHNIKER
A-8350 FEHRING, GRÜNE LAGUNE 2, TEL. +43 3155/5122, FAX DW 66

GESAMT-LAGEPLAN / AUSSENANLAGEN



BGF BERECHNUNG:	
OG F1: 13,99x8,97=125,49m ² SUMME OG: 125,49m ²	
WNF: 254,29m ²	
EG F1: 13,99x8,97=125,49m ² F2: 6,00x8,02=48,12m ² SUMME EG: 161,61m ²	
GESAMTNUTZFLÄCHE: 299,40m ²	
KG F1: 13,99x8,97=125,49m ² SUMME KG: 125,49m ²	
GRUNDSTÜCKSFLÄCHE: 1230m ²	
SUMME BGF: 412,59m ²	
SUMME BGF ohne Keller: 287,10m ²	
BEBAUUNGSDICHTE: 0,250	
BEBAUUNGSGRAD : 0,2334146	

AUSSENANLAGEN 1/500

NEUBAU WOHNHAUS DR. TRIFU
GZ: 26500


6.06.2007
INDEX A

MAßSTAB 1/500
GRUNDRISS

ARCHITEKTEN CSERNI & PAUGGER ZIVILTECHNIKER GmbH
STAATLICH BEFUGTE UND BEEIDETE ZIVILTECHNIKER
A-8350 FEHRING, GRÜNE LAGUNE 2, TEL. +43 3155/5122, FAX DW 66



GRUNDRISS KELLERGEOSCHOSS

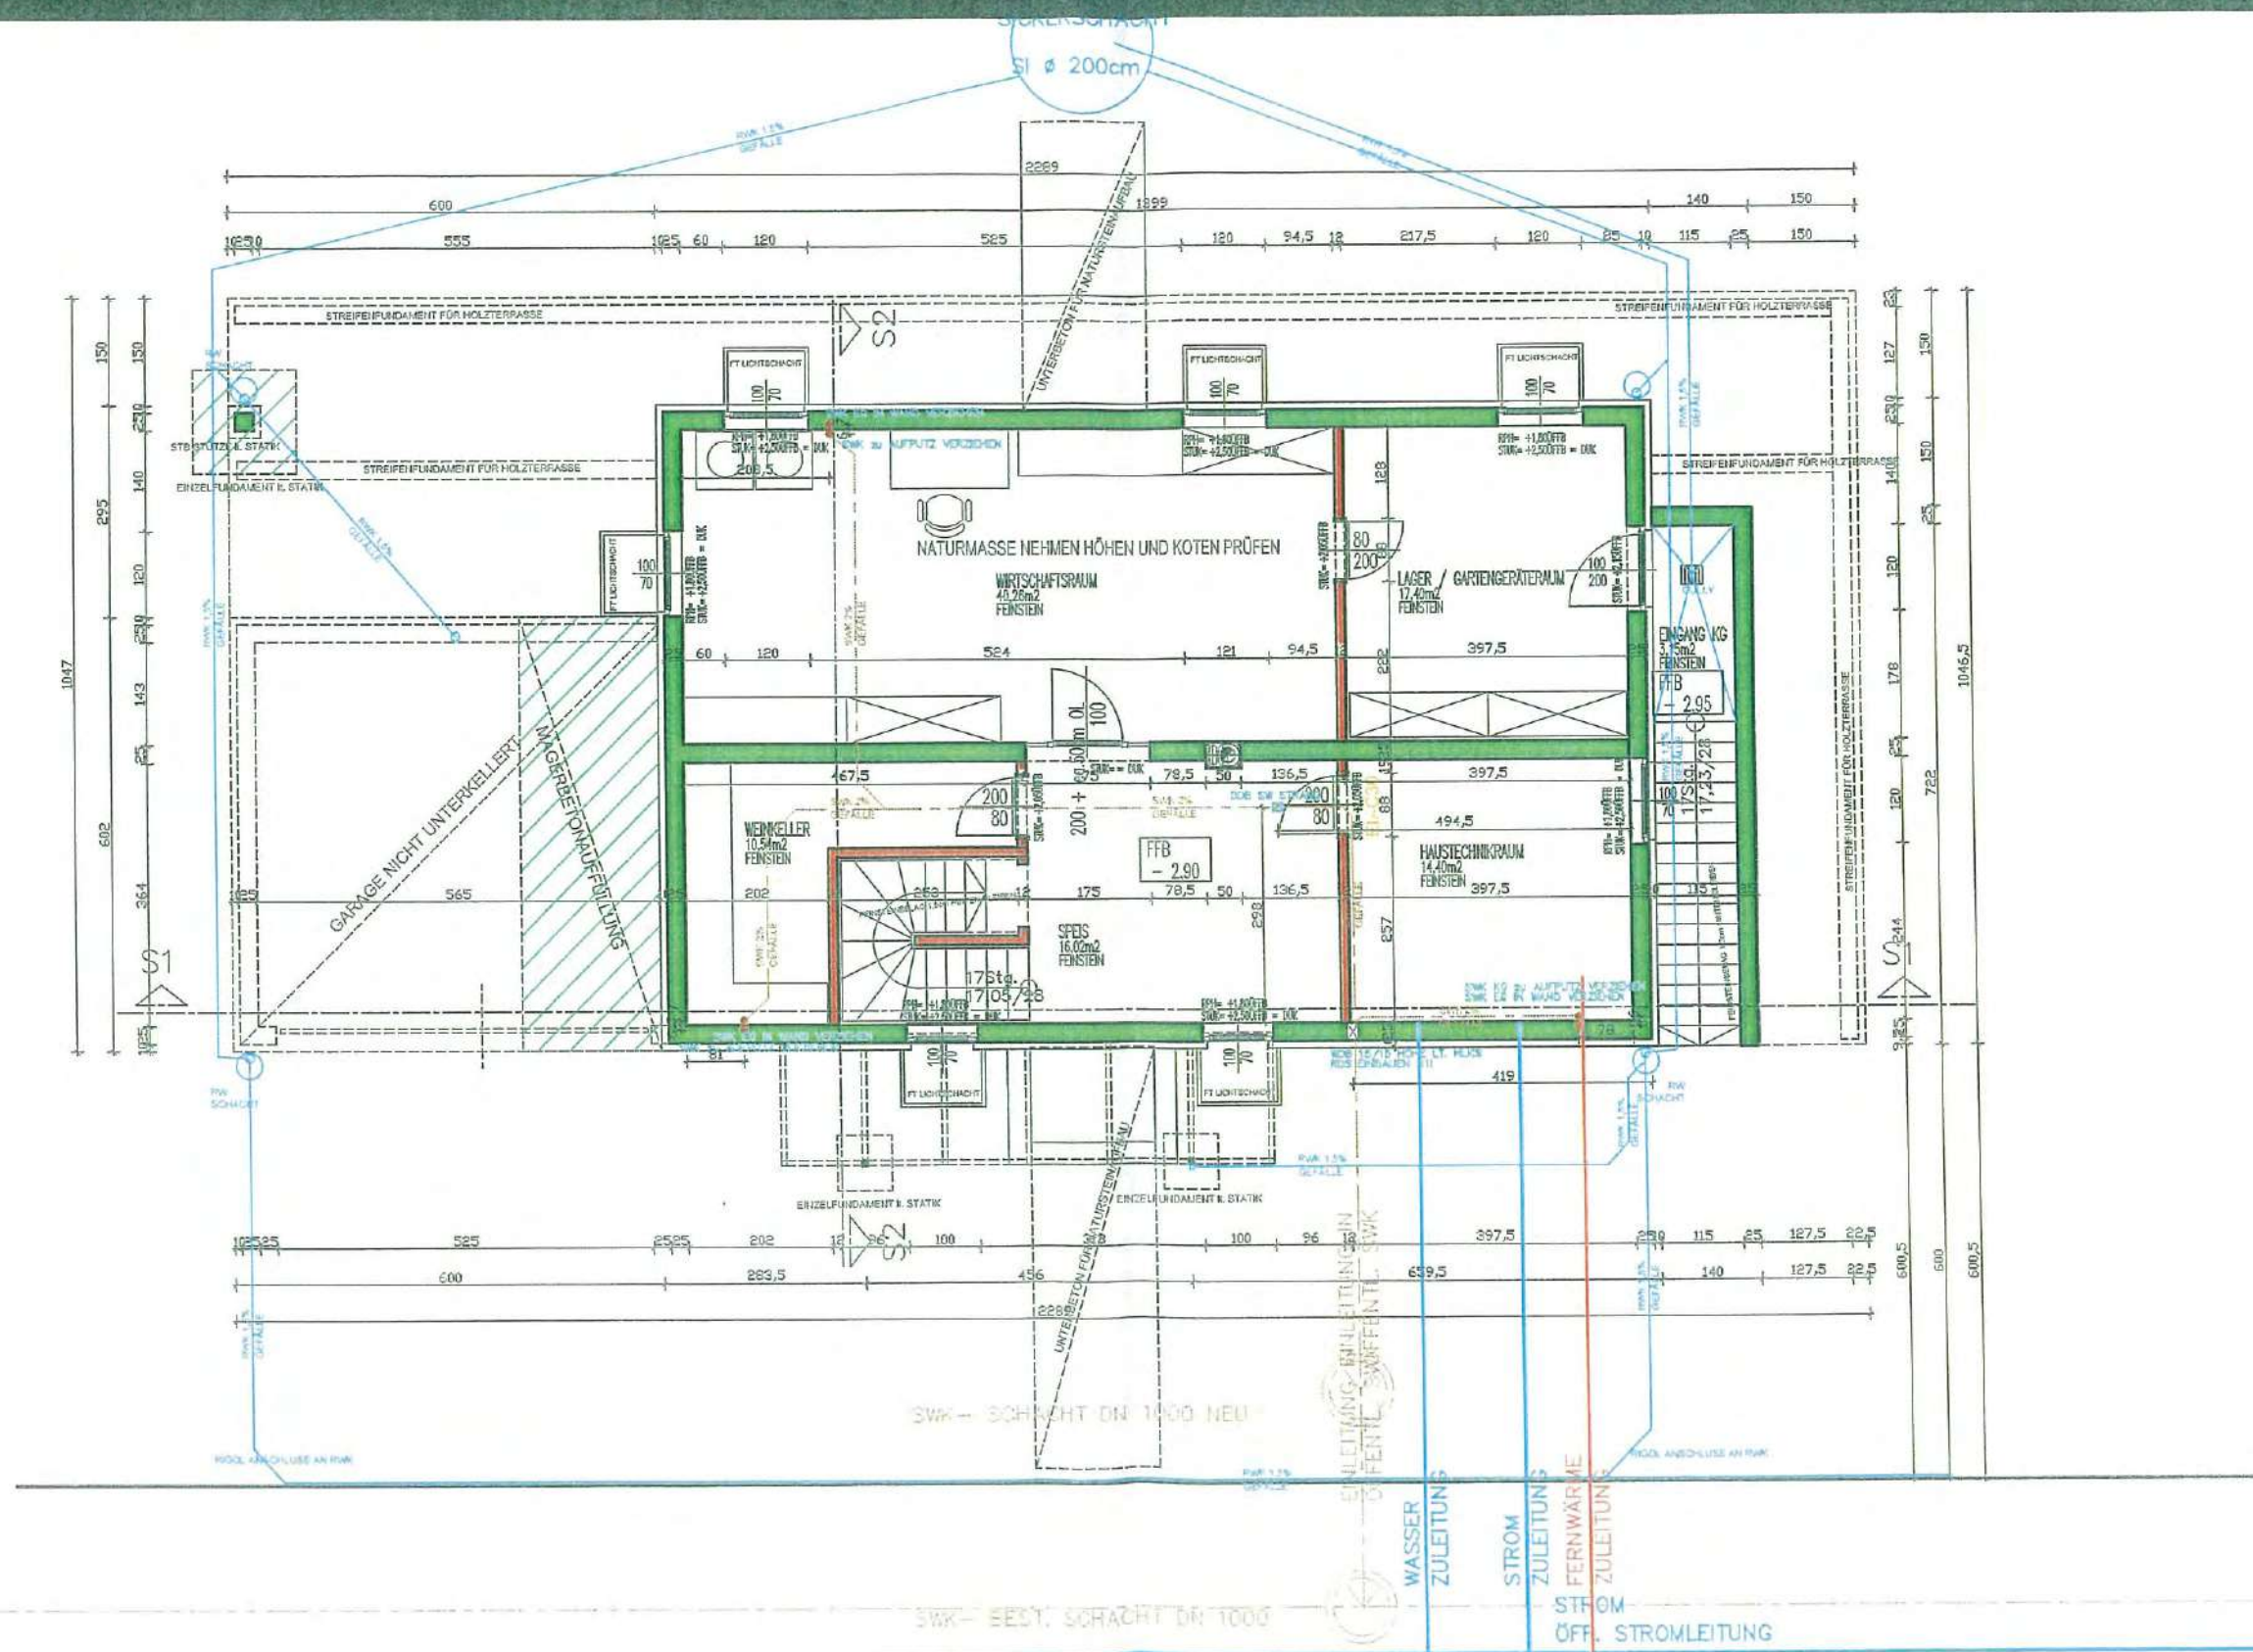

NEUBAU WOHNHAUS DR. TRIFU
GZ: 26500


6.06.2007
INDEX B

MAßSTAB 1:100
GRUNDRISS

ARCHITEKTEN CSERNI & PAUGGER ZIVILTECHNIKER GmbH
STAATLICH BEFUGTE UND BEEIDETE ZIVILTECHNIKER
A-8350 FEHRING, GRÜNE LAGUNE 2, TEL. +43 3155/5122, FAX DW 66



GRUNDRISS ERDGESCHOSS

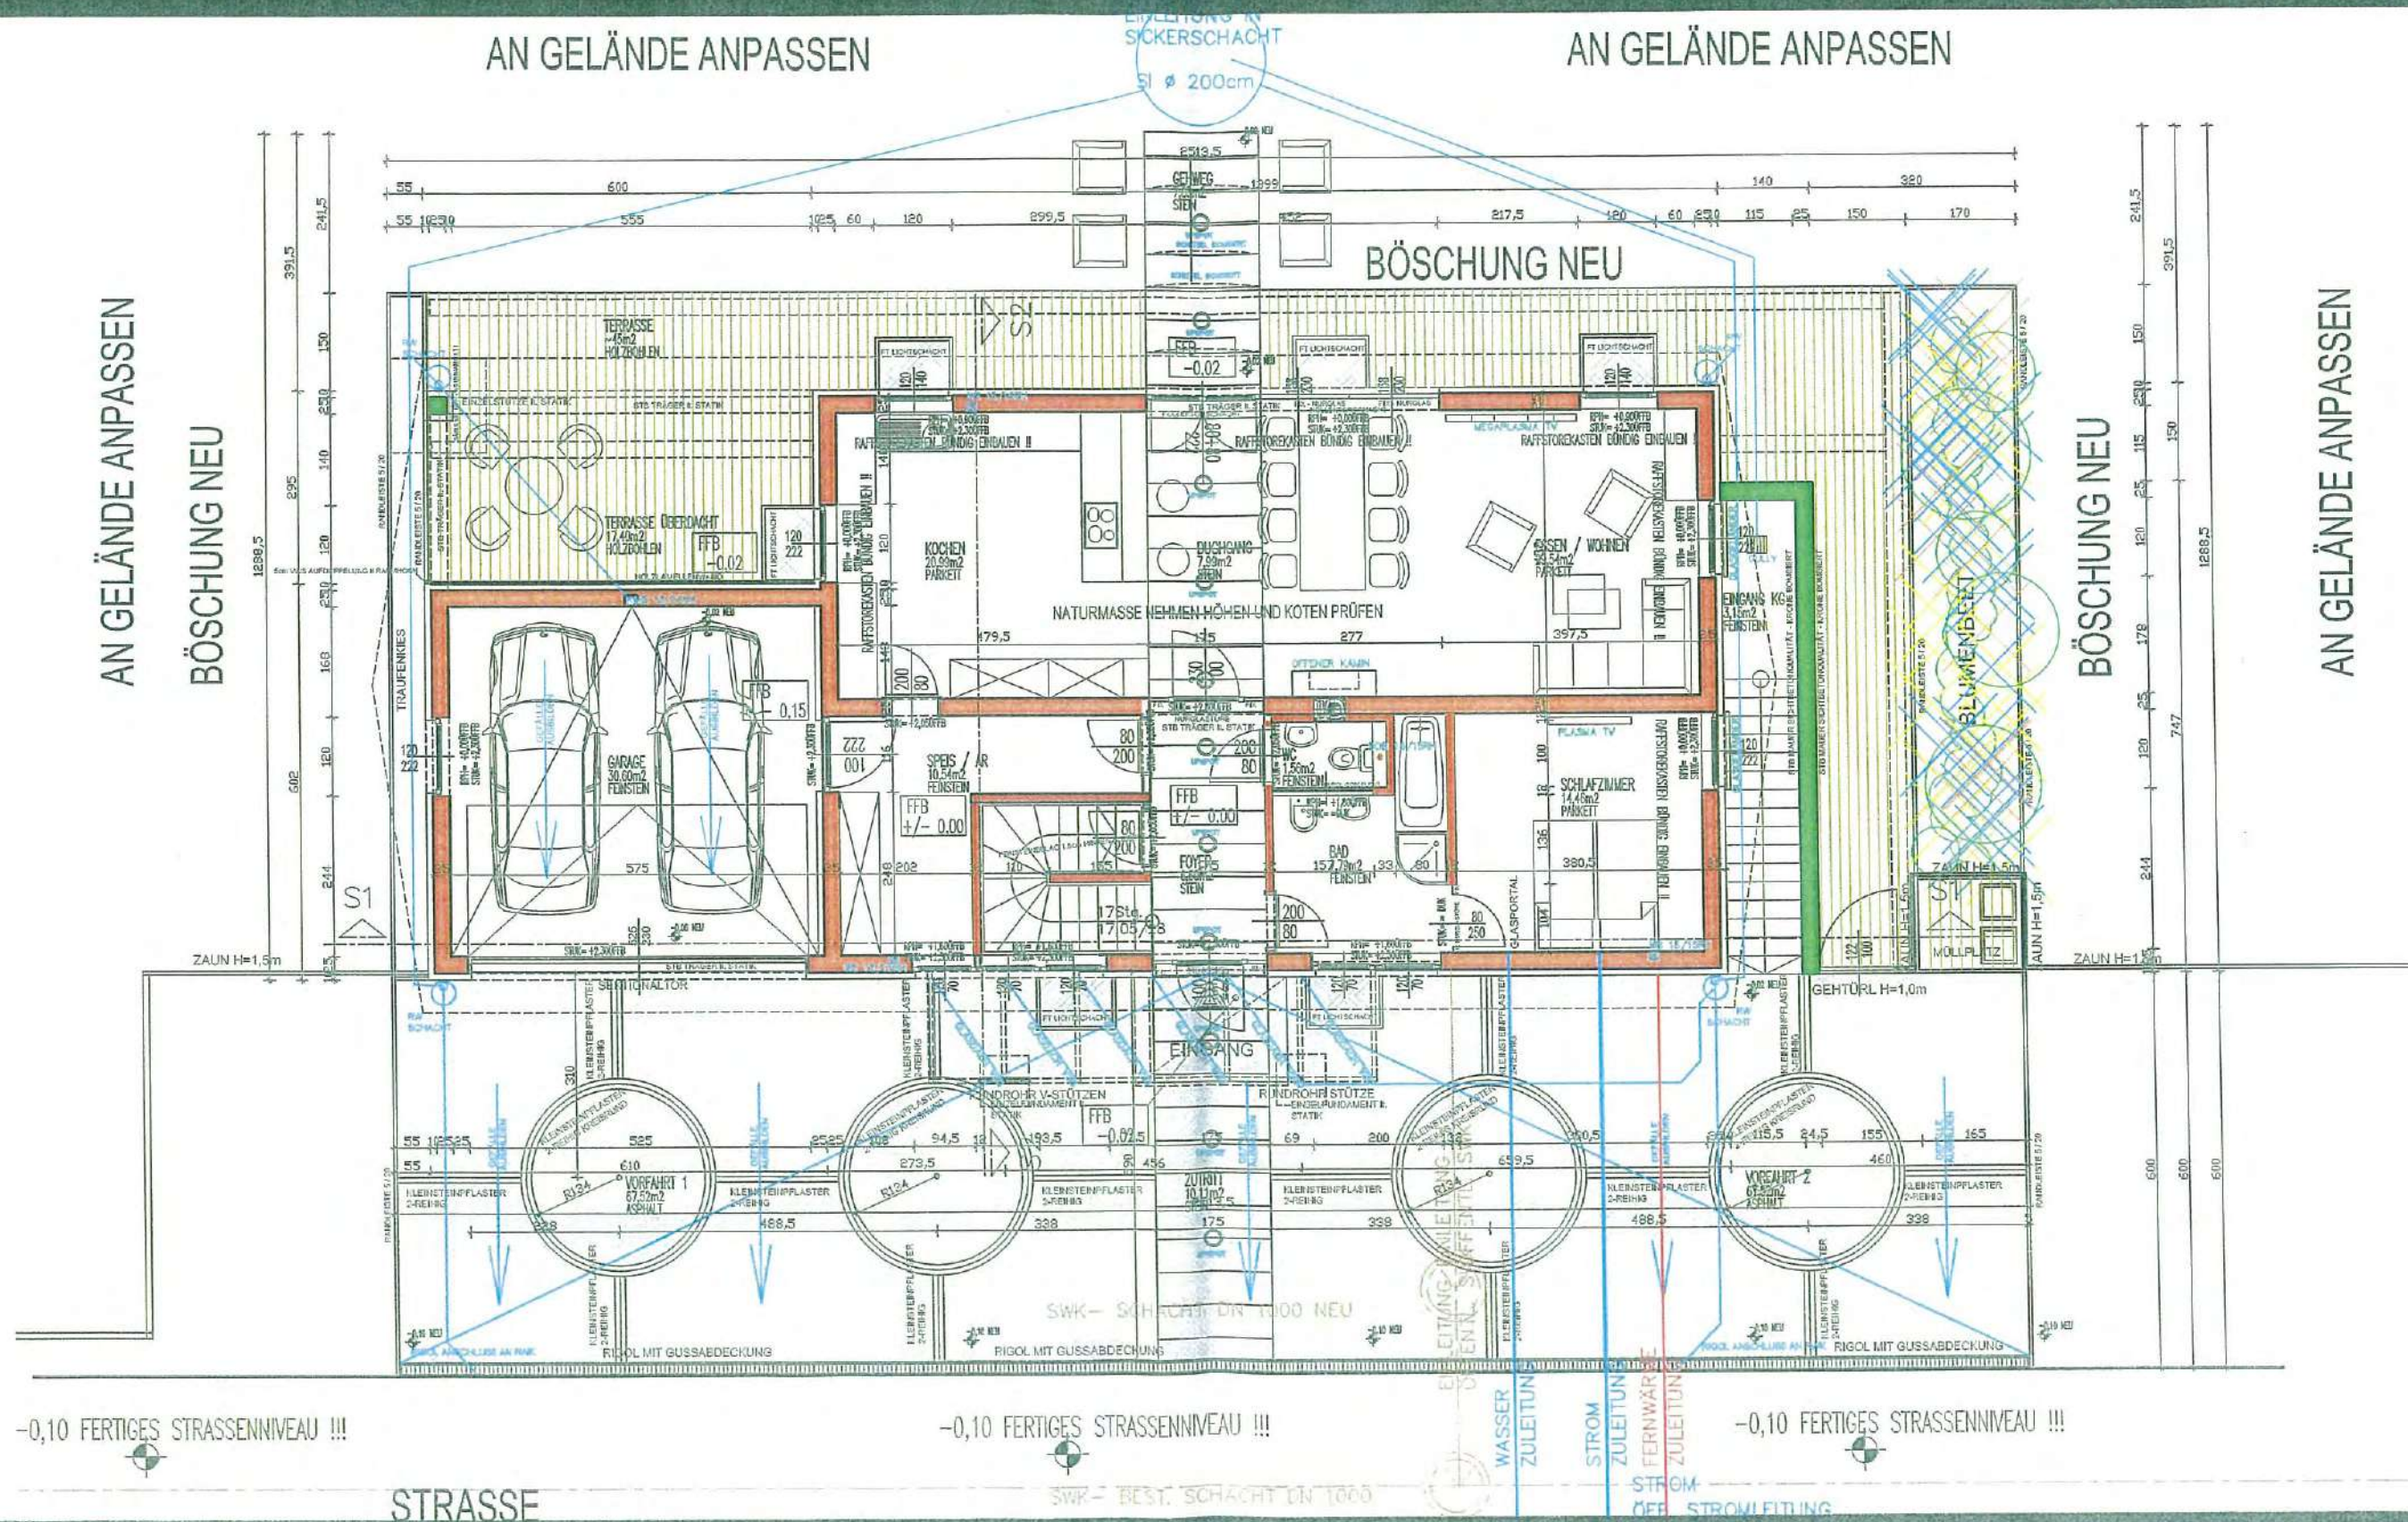

NEUBAU WOHNHAUS DR. TRIFU
GZ: 26500

6.6.2007
INDEX B


MAßSTAB 1:100
GRUNDRISS

ARCHITEKTEN CSERNI & PAUGGER ZIVILTECHNIKER GmbH



STAATLICH BEFUGTE UND BEEIDETE ZIVILTECHNIKER
A-8350 FEHRING, GRÜNE LAGUNE 2, TEL. +43 3155/5122, FAX DW 66

GRUNDRISS 1.OBERGESCHOSS

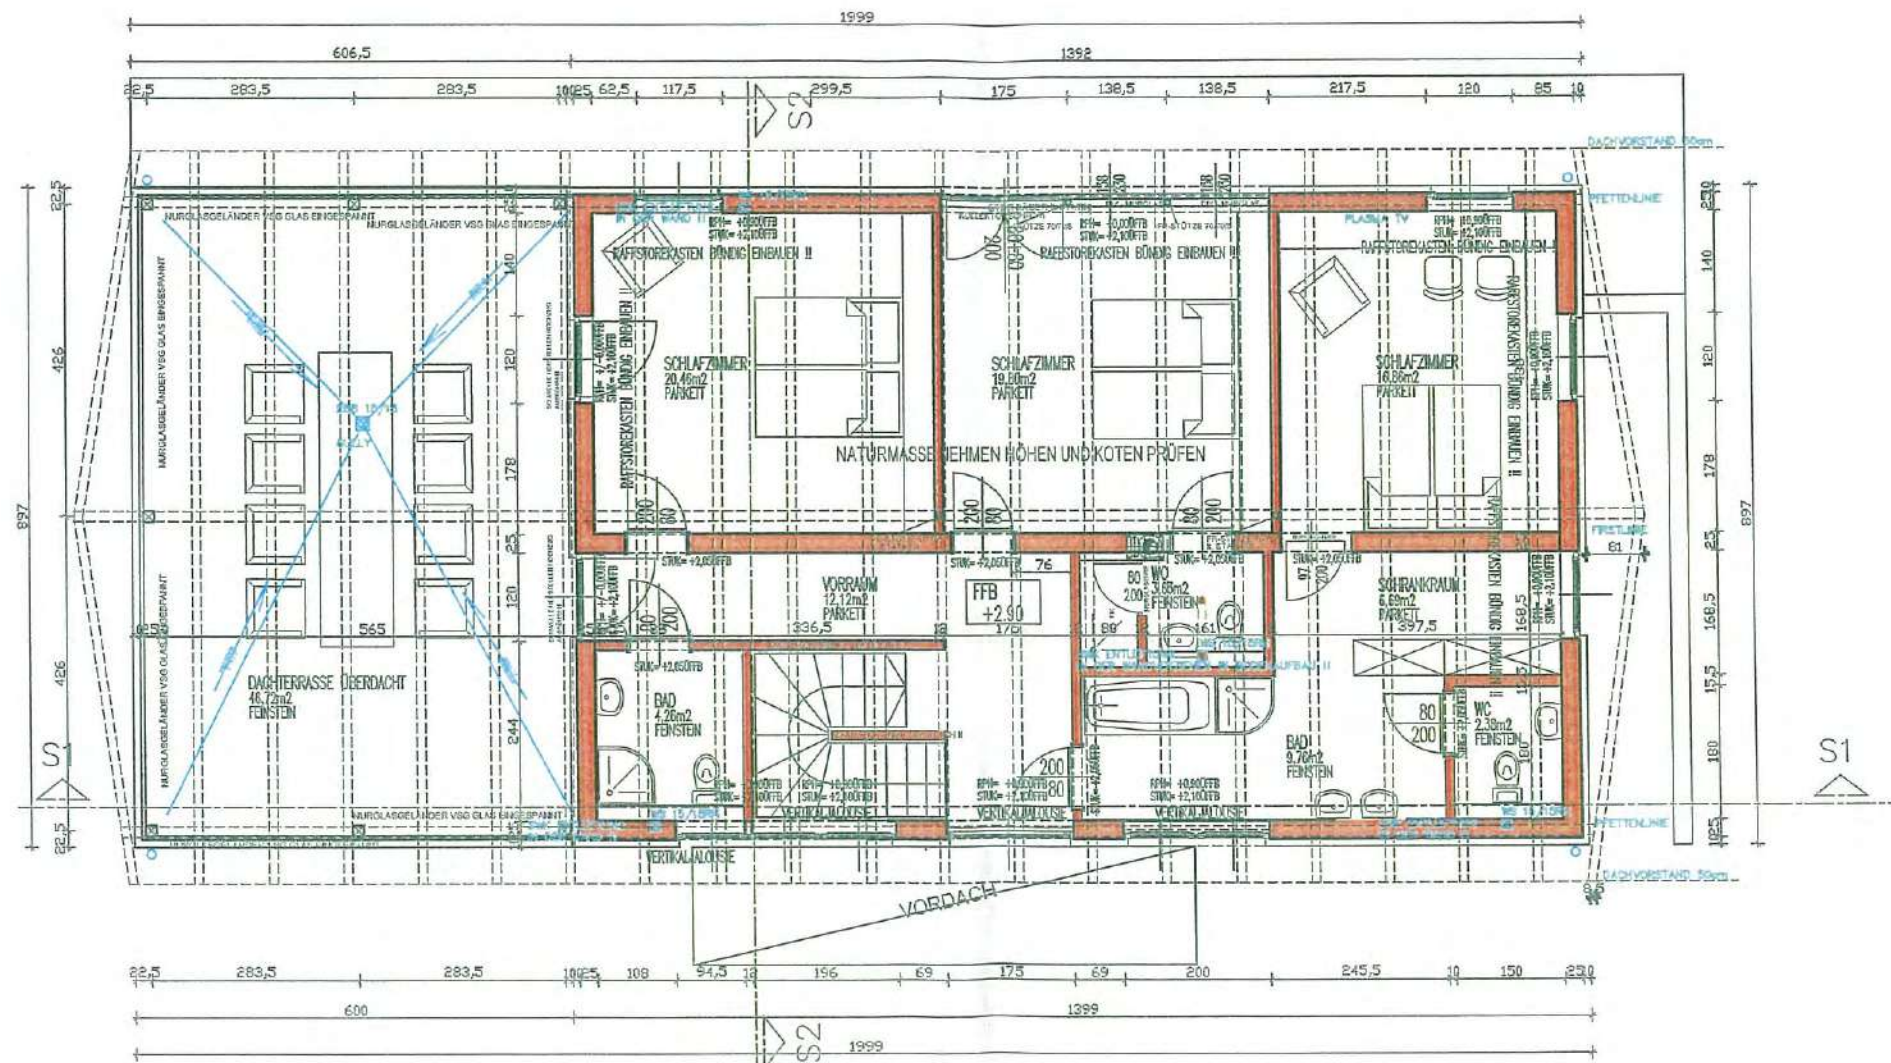


NEUBAU WOHNHAUS DR. TRIFU
GZ: 26500

6.6.2007
INDEX B


MAßSTAB 1:100
GRUNDRISS

ARCHITEKTEN CSERNI & PAUGGER ZIVILTECHNIKER GmbH
STAATLICH BEFUGTE UND BEEIDETE ZIVILTECHNIKER
A-8350 FEHRING, GRÜNE LAGUNE 2, TEL. +43 3155/5122, FAX DW 66


SCHNITT S1

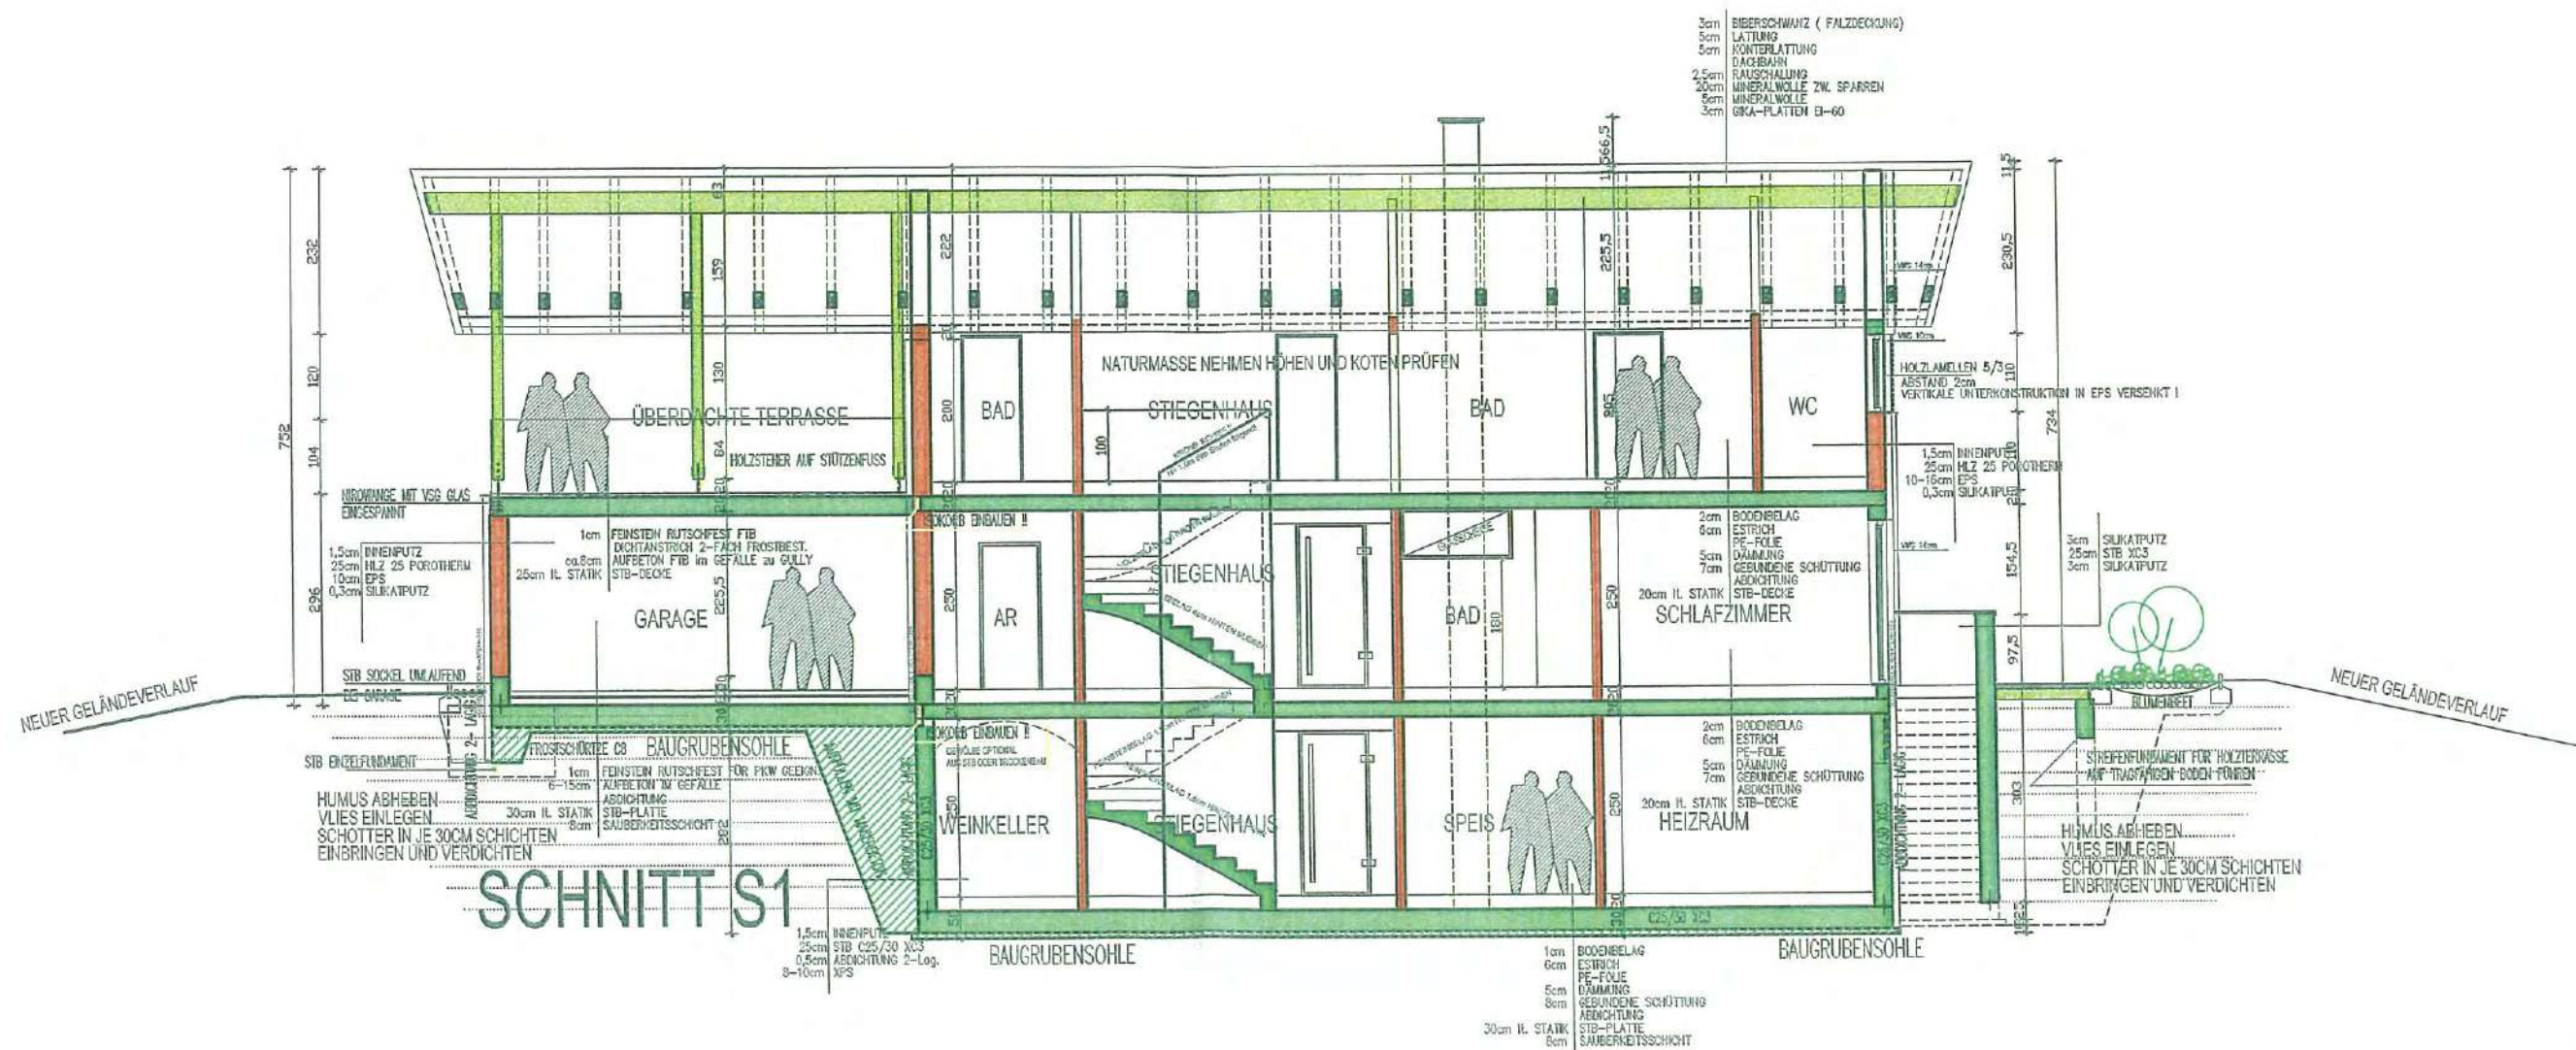

SCHNITT S2

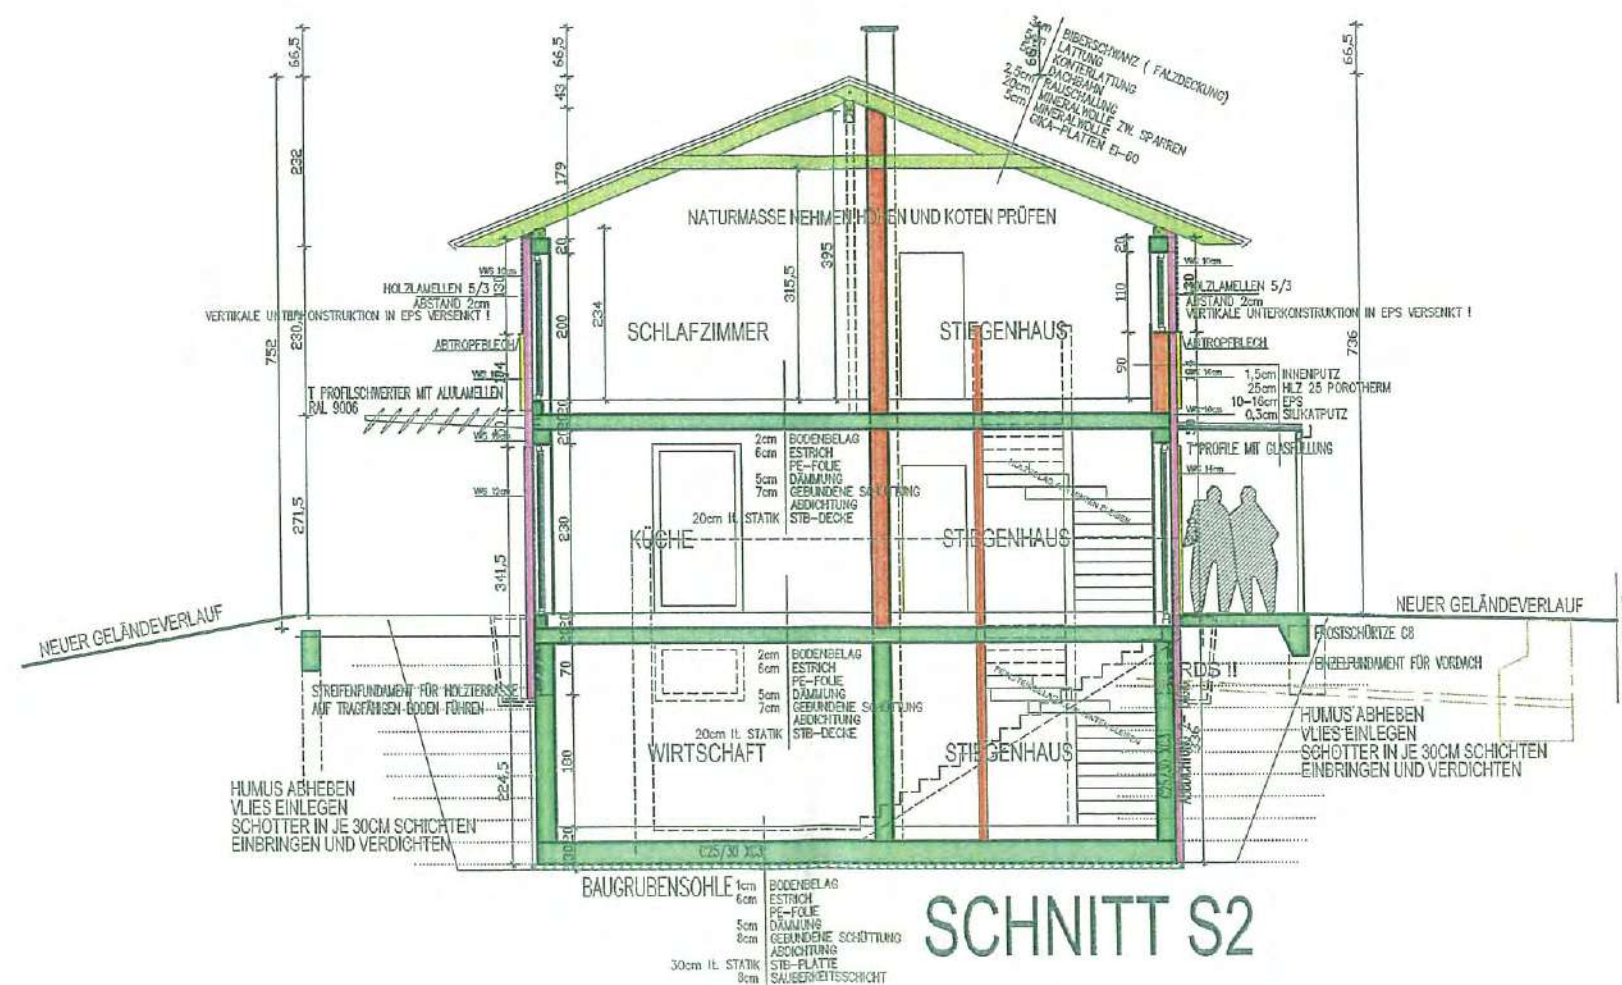

ANSICHT NORDEN

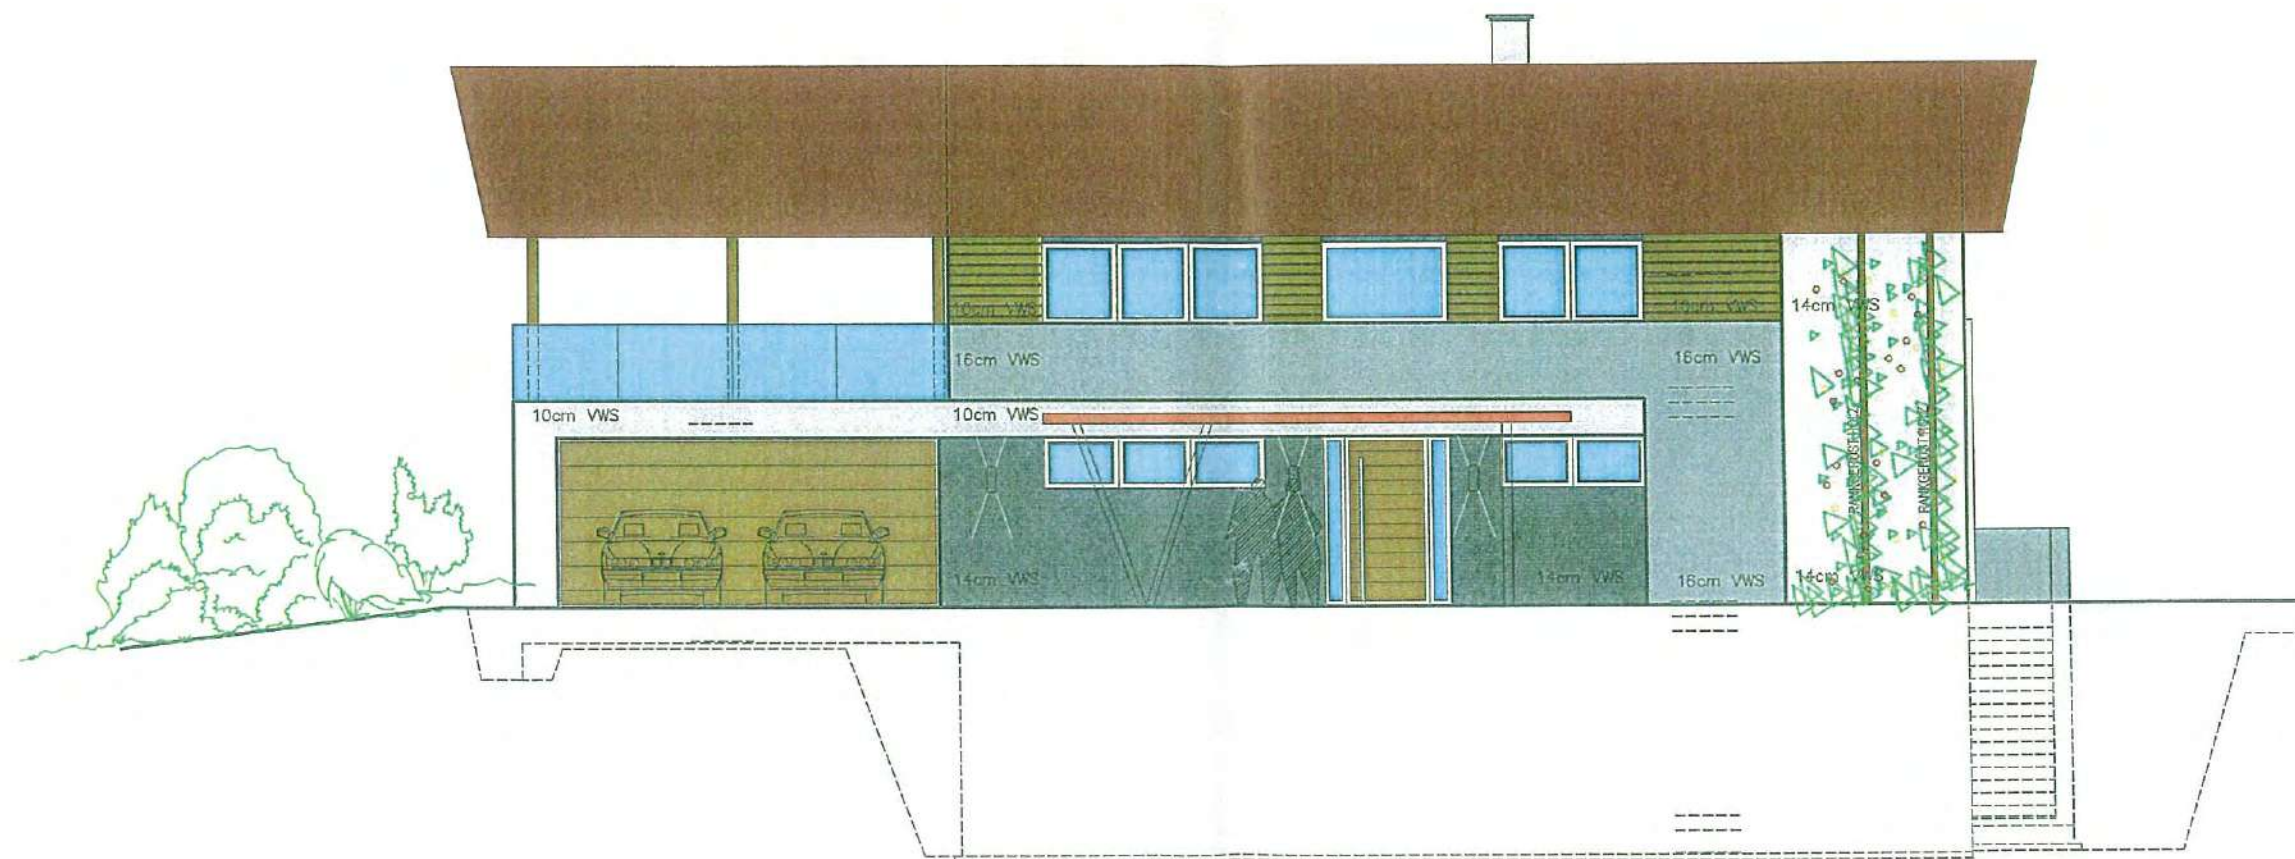


NEUBAU WOHNHAUS DR. TRIFU
GZ: 26500

6.6.2007
INDEX A

MAßSTAB 1/100
ANSICHT

ARCHITEKTEN CSERNI & PAUGGER ZIVILTECHNIKER GmbH
ZT
STAATLICH BEFUGTE UND BEEIDETE ZIVILTECHNIKER
A-8350 FEHRING, GRÜNE LAGUNE 2, TEL. +43 3155/5122, FAX DW 66

ANSICHT OSTEN

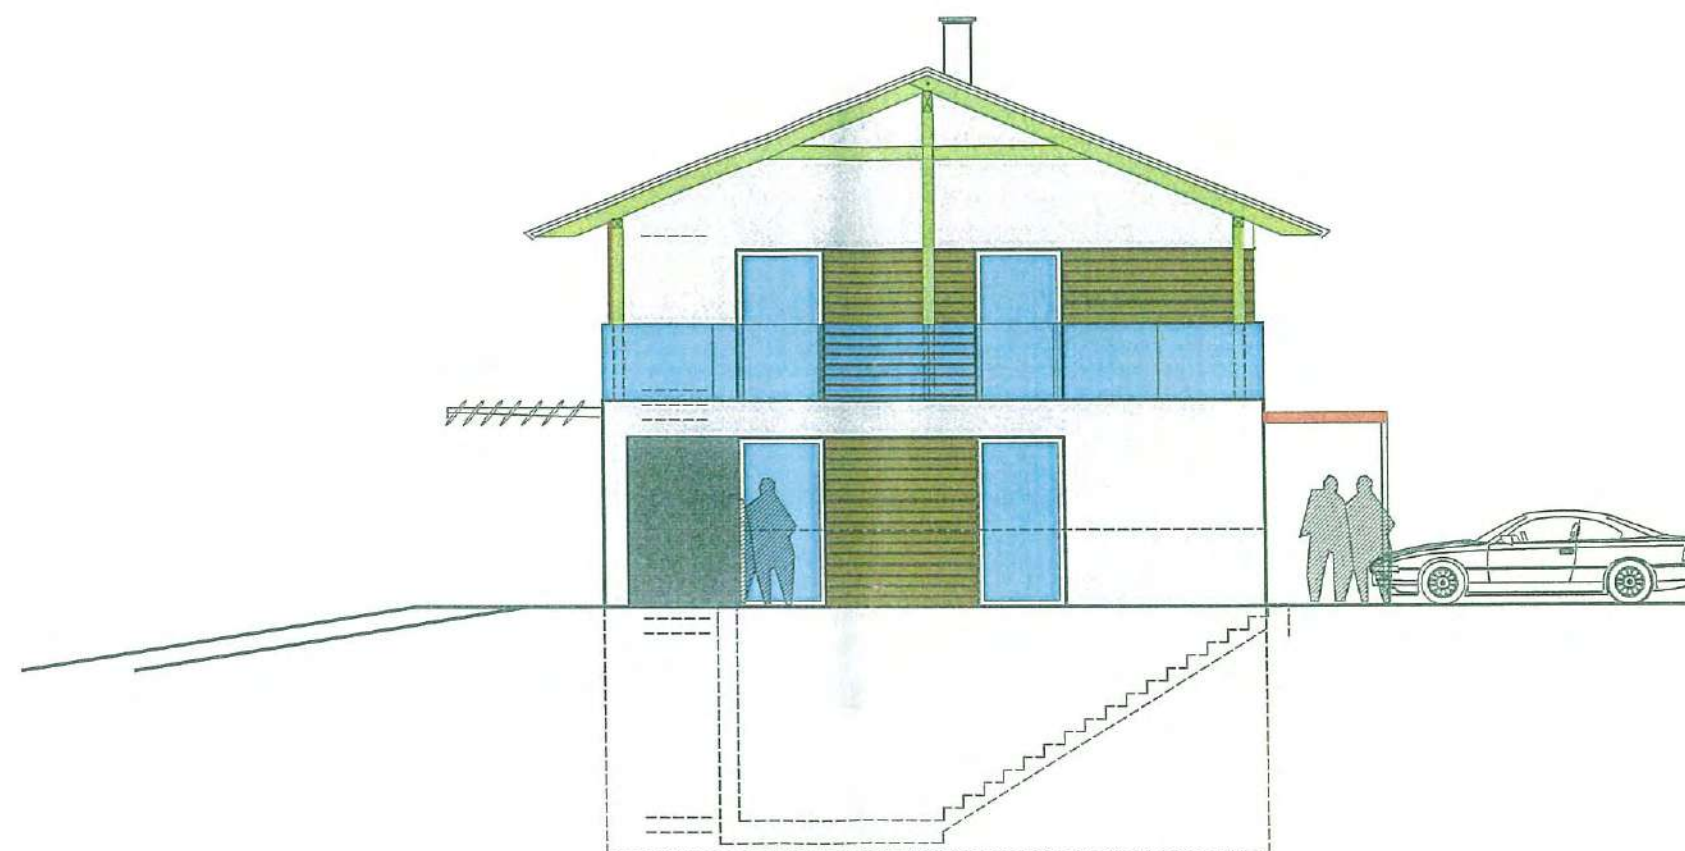

NEUBAU WOHNHAUS DR. TRIFU
GZ: 26500

6.6.2007
INDEX A


MAßSTAB 1/100
ANSICHTEN

ARCHITEKTEN CSERNI & PAUGGER ZIVILTECHNIKER GmbH



STAATLICH BEFUGTE UND BEEIDETE ZIVILTECHNIKER
A-8350 FEHRING, GRÜNE LAGUNE 2, TEL. +43 3165/5122, FAX DW 66

ANSICHT WESTEN

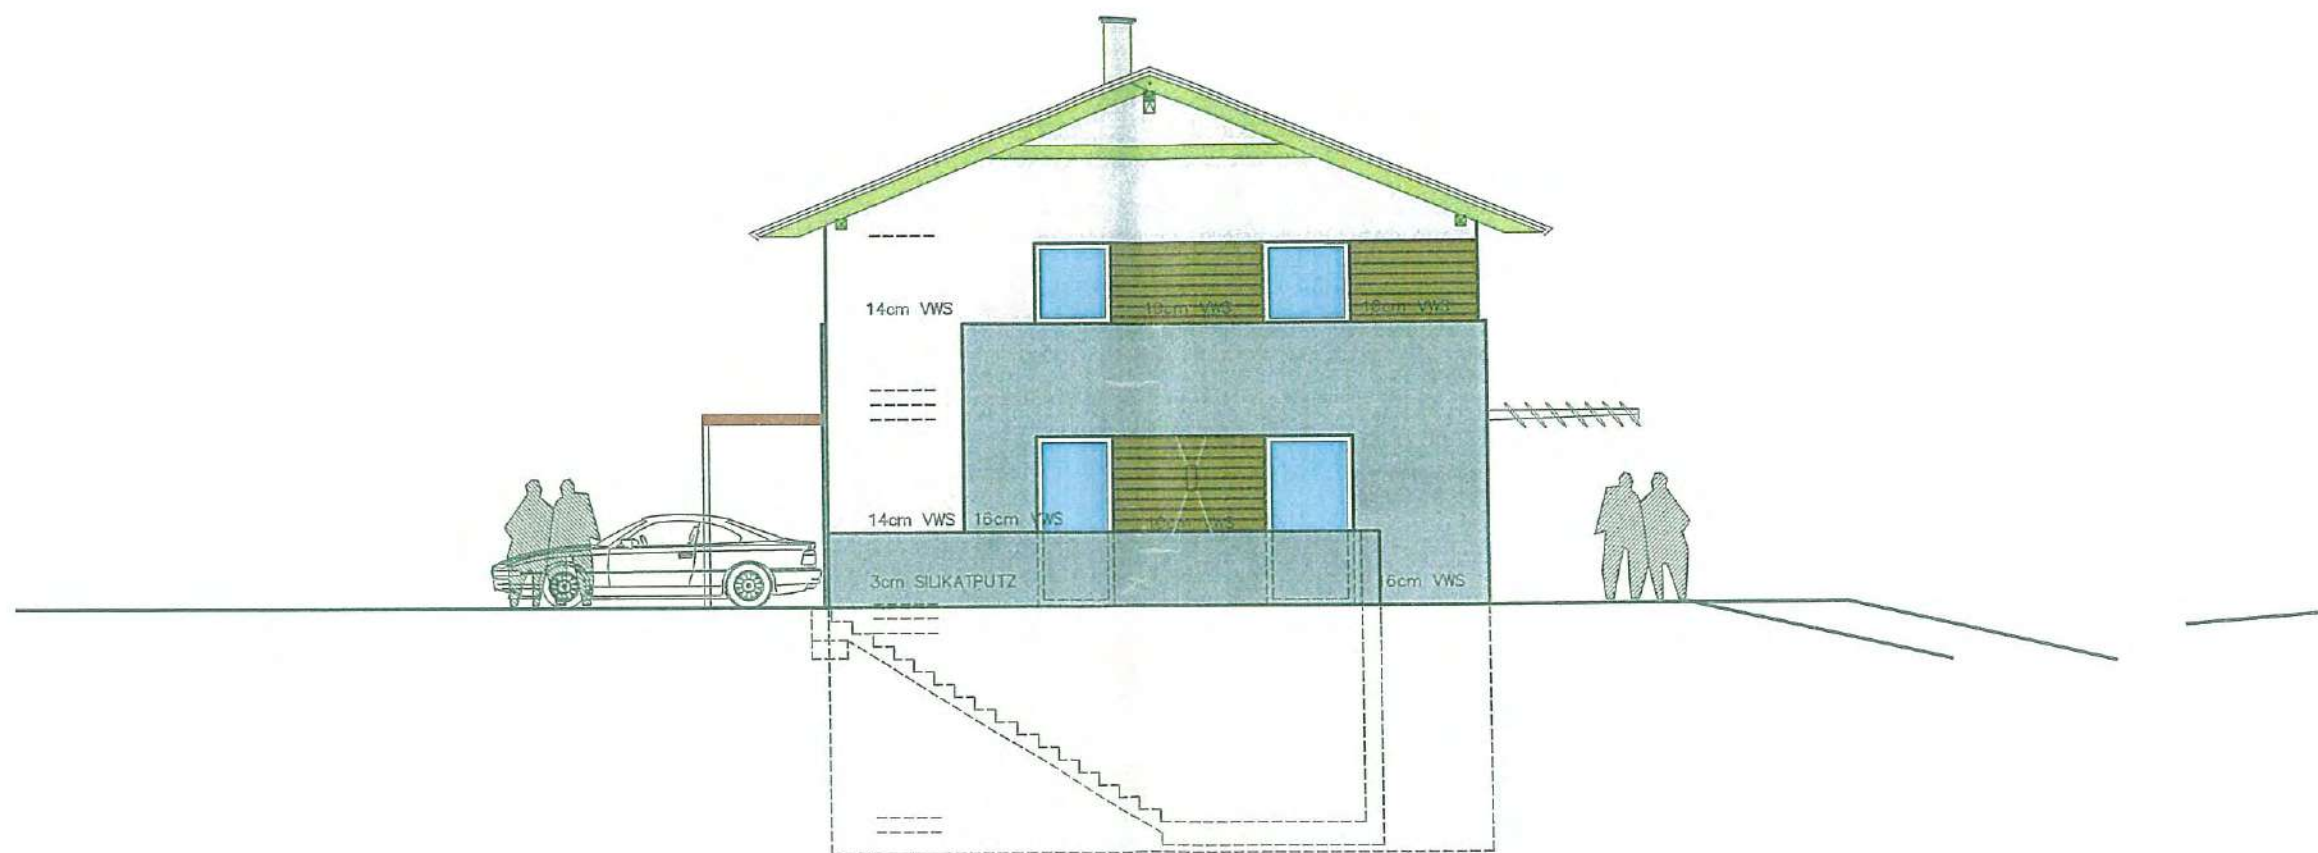

NEUBAU WOHNHAUS DR. TRIFU
GZ: 26500

6.06.2007
INDEX A

MAßSTAB 1/100
ANSICHTEN

ARCHITEKTEN CSERNI & PAUGGER ZIVILTECHNIKER GmbH
STAATLICH BEFUGTE UND BEEIDETE ZIVILTECHNIKER
A-8350 FEHRING, GRÜNE LAGUNE 2, TEL. +43 3155/5122, FAX DW 66

